
The Intersection |Bridging GBA Tech & Hong Kong Capital


Smart Transit-Oriented Development Design Studio

Team Members
LU Yutian, LIN Meigu, LING Yuxiang, GU Xinyan


1 Macro-scale: Regional Synergy & AI Policy Support

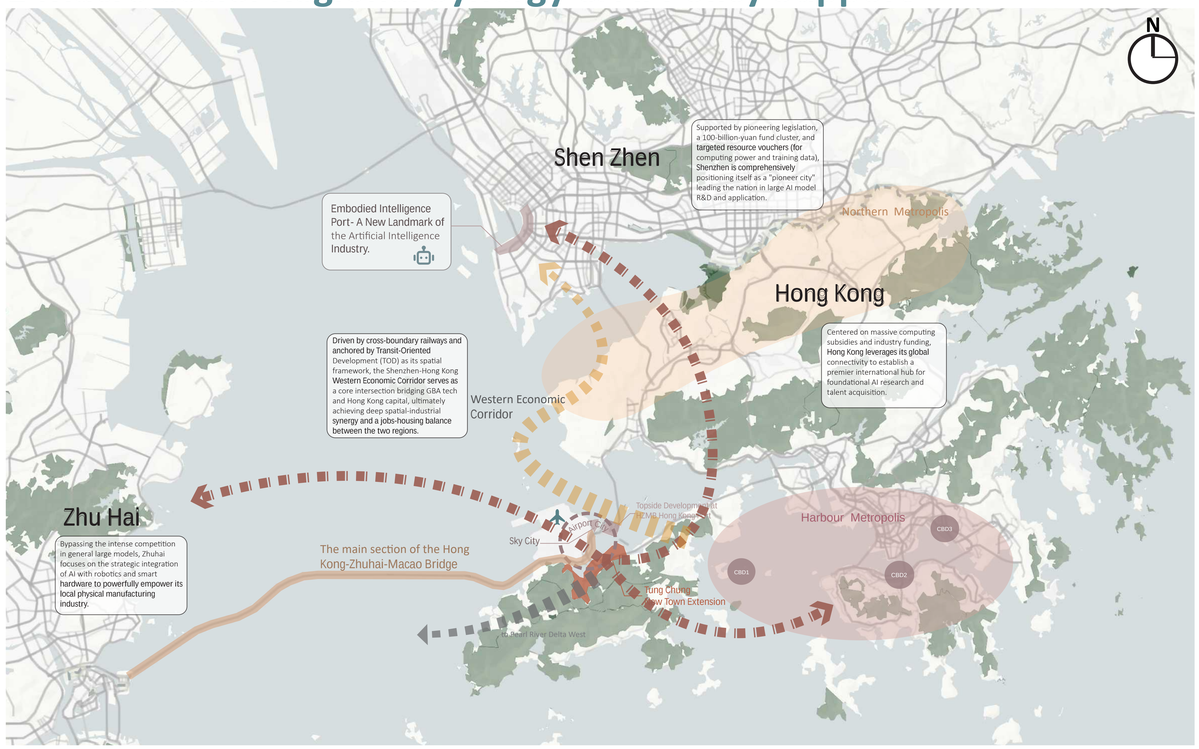


2 Meso-scale: Strategic Transit & Unique Leisure

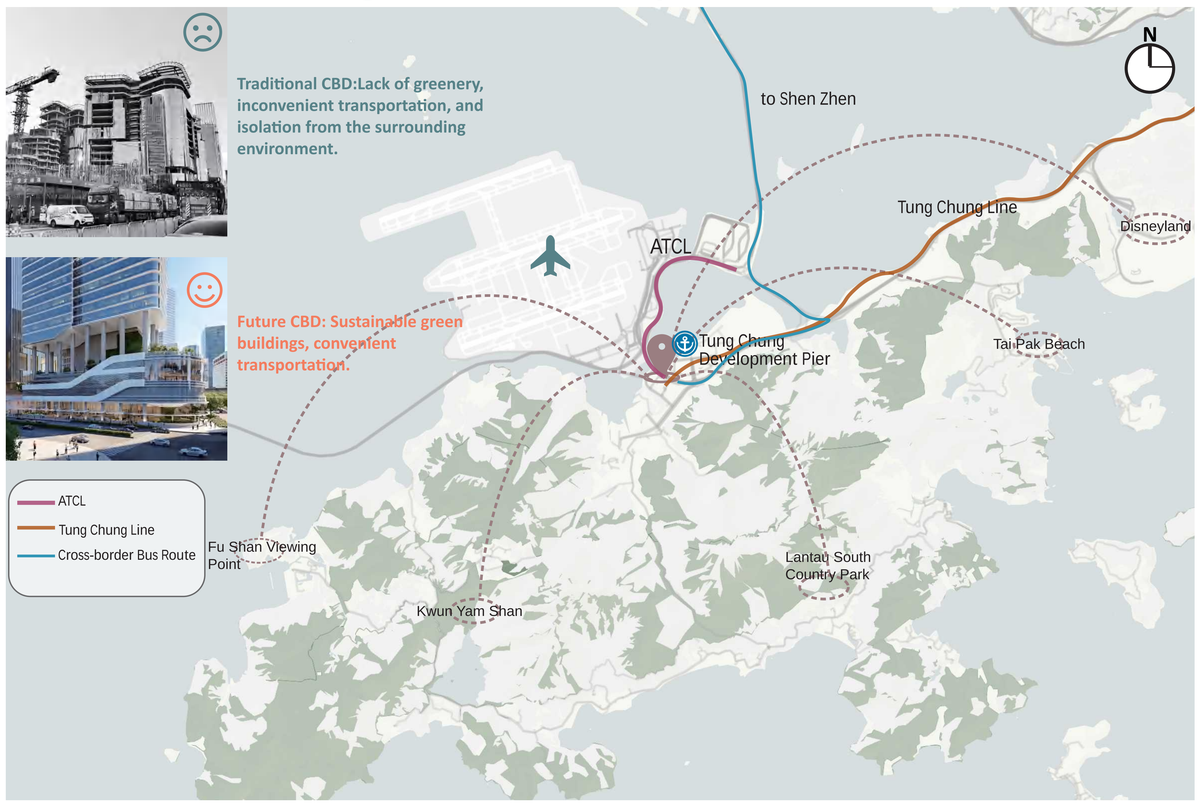


3 Poor Pedestrian Accessibility

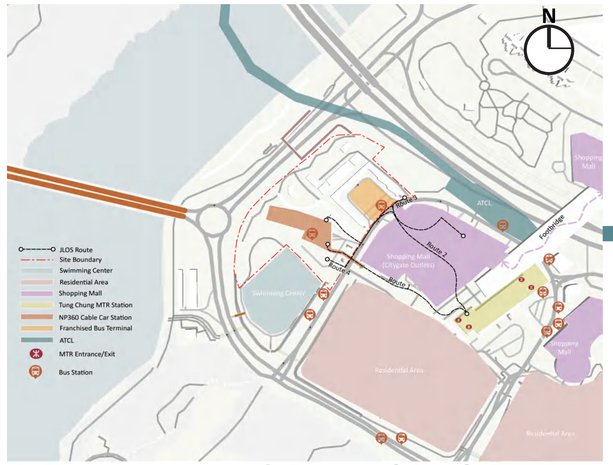


4 Disconnected Spatial Linkages

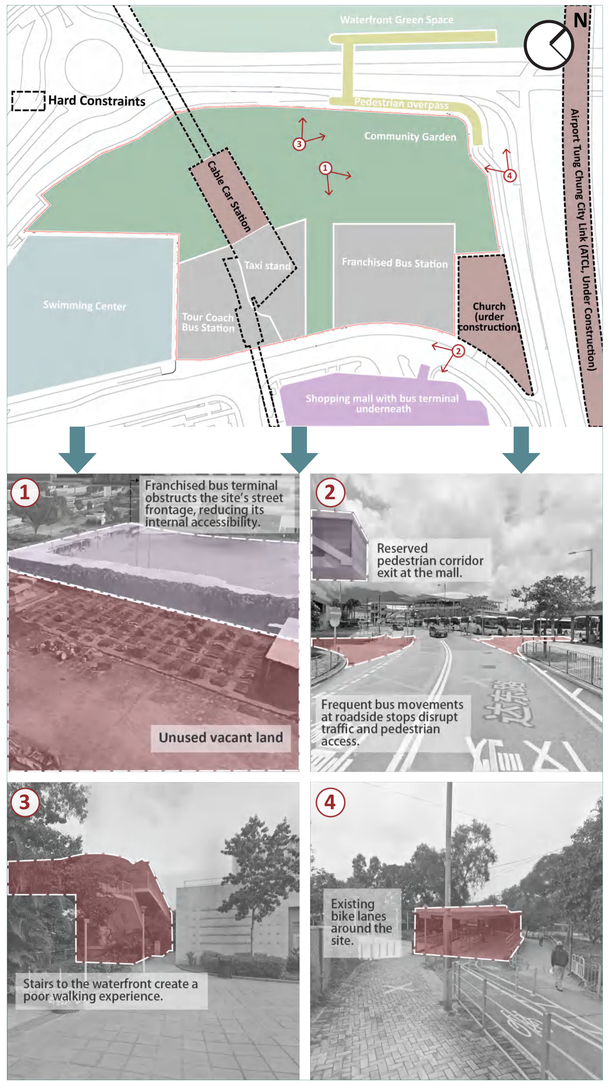


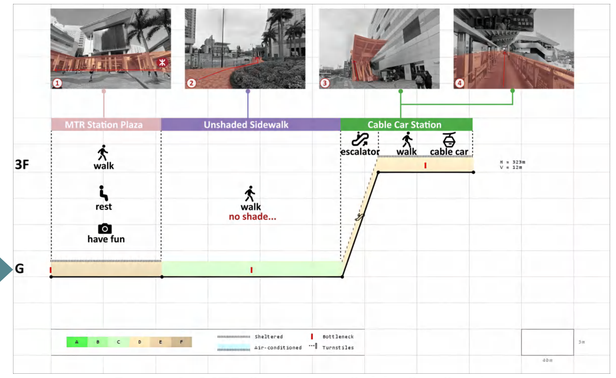


Route 1: MTR Station → Cable Car Station

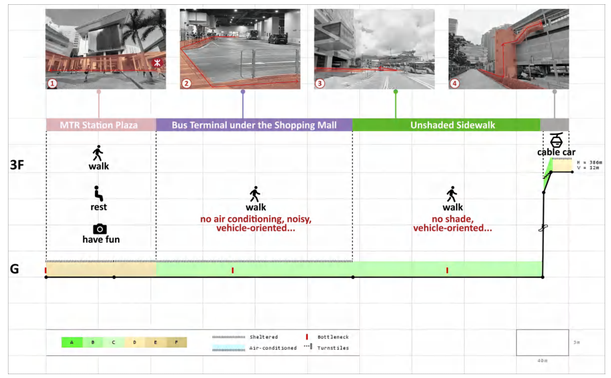

Route 2: MTR Station → Bus Terminal → Cable Car Station

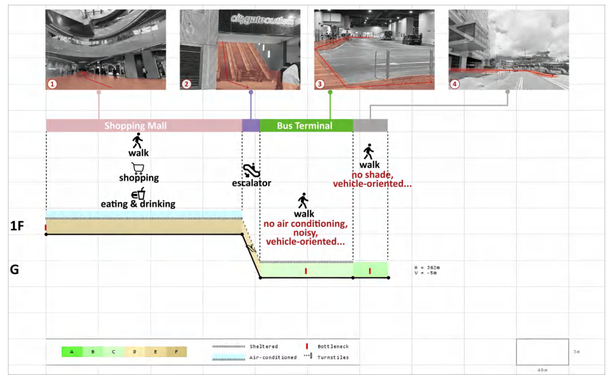

Route 3: 1F of Shopping Mall → Franchised Bus Station

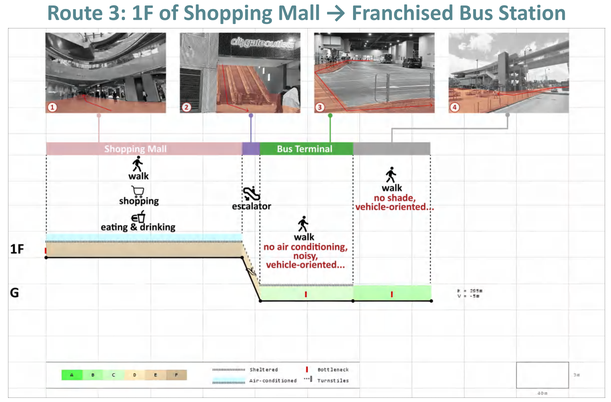


Route 4: 1F of Shopping Mall → Tour Coach Bus Station

The Intersection | Bridging GBA Tech & Hong Kong Capital

Smart Transit-Oriented Development Design Studio

Team Members
LU Yutian, LIN Meigu, LING Yuxiang, GU Xinyan


5 Severe Pedestrian-Vehicle Conflict

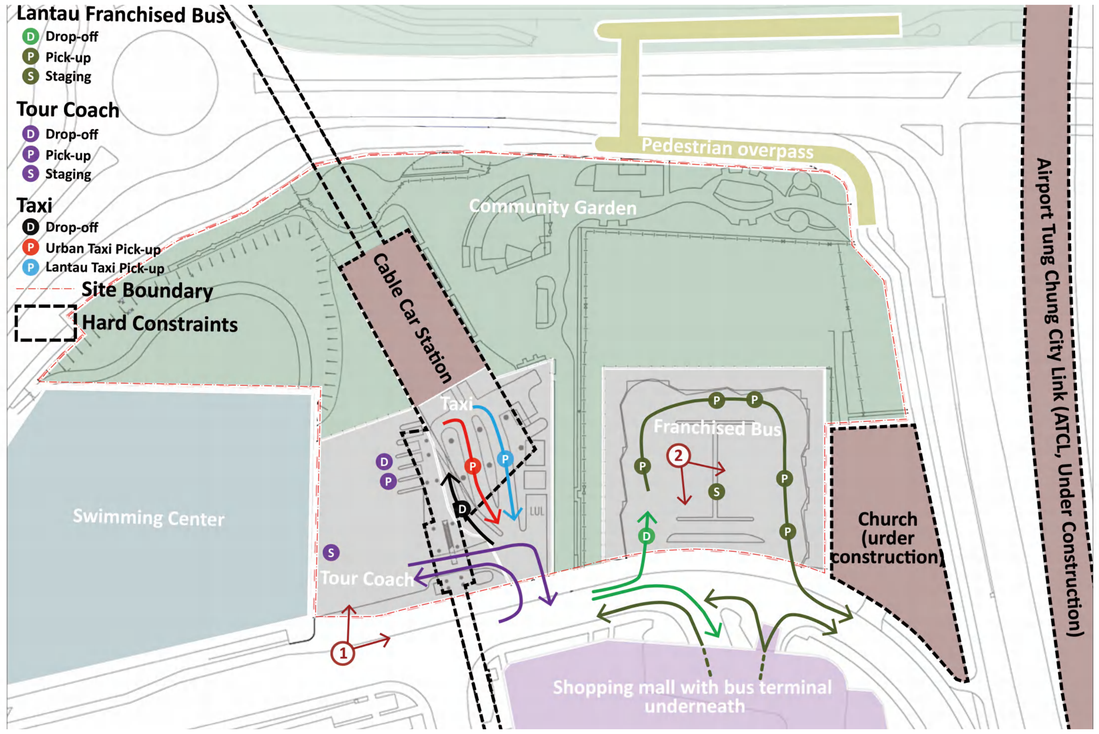






6 Design Concept

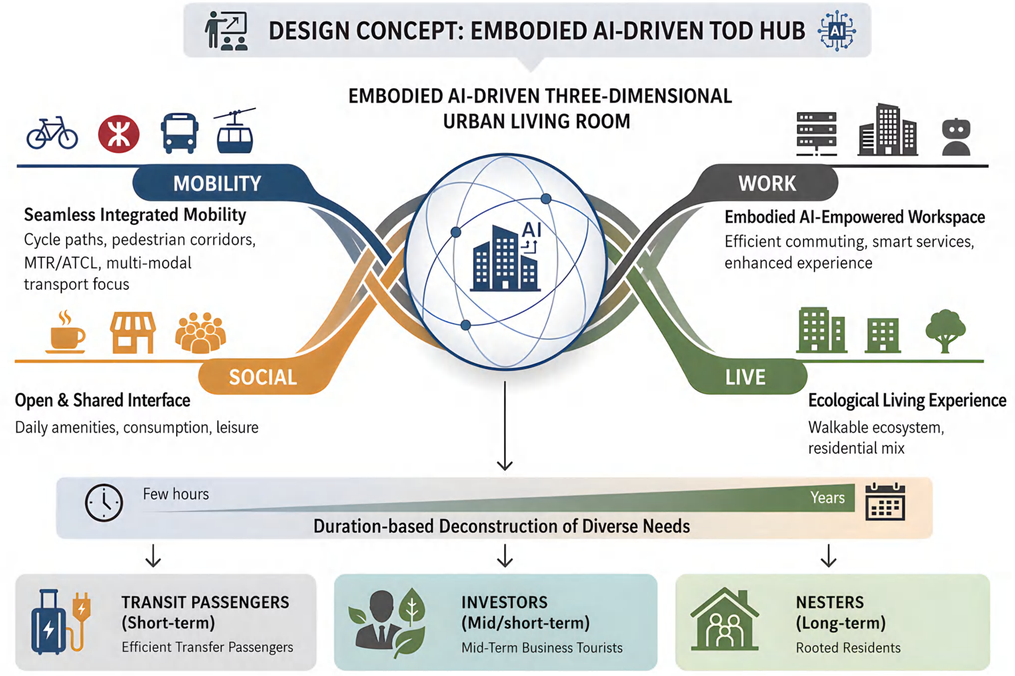

7 Target User Analysis

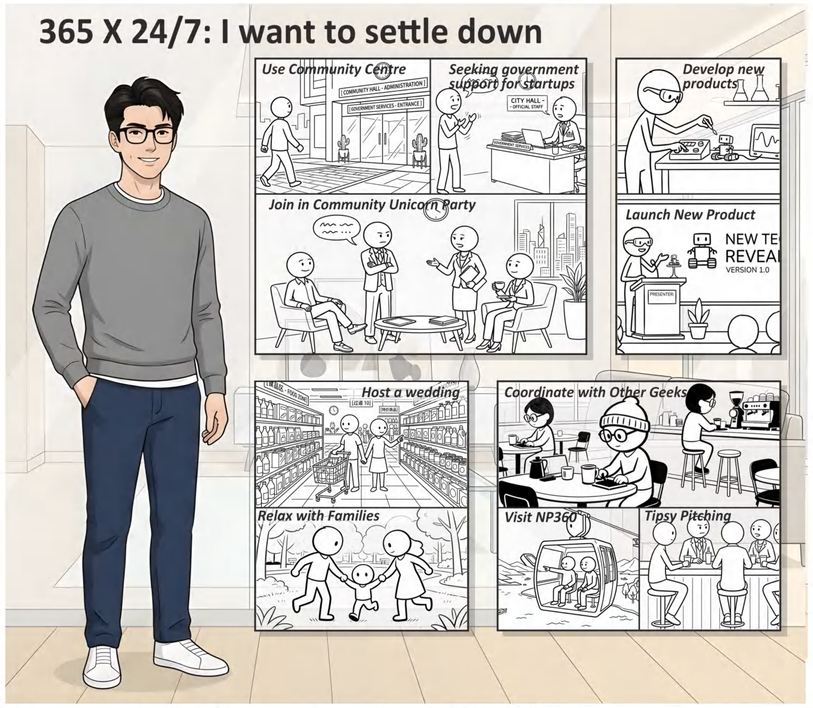


Nesters & Public—— Work & Life Balance

LIFE | WORK | SOCIAL | MOBILITY



Business People—— A Bleisure Trip


LIFE | WORK | SOCIAL | MOBILITY

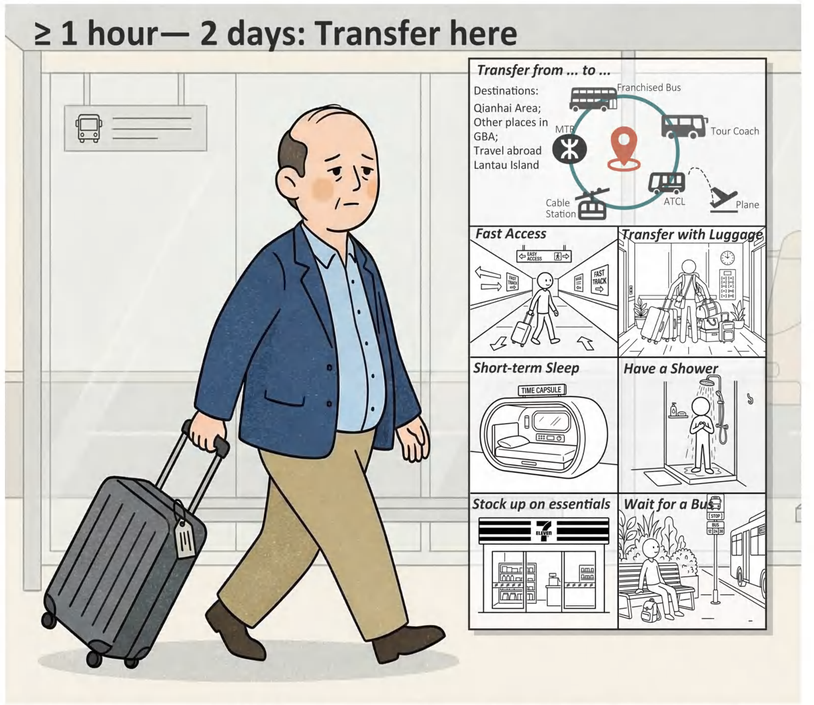


Travelers—— Efficient Transfer, Need to Recharge!

LIFE | WORK | SOCIAL | MOBILITY


8 Design Strategy

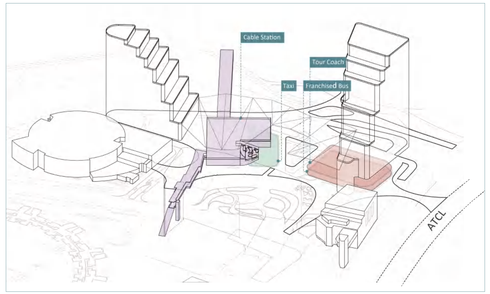


Centralize Mobility

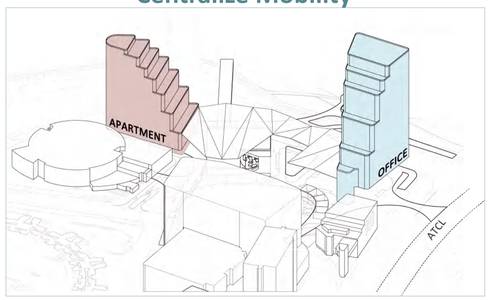

Integrate Development

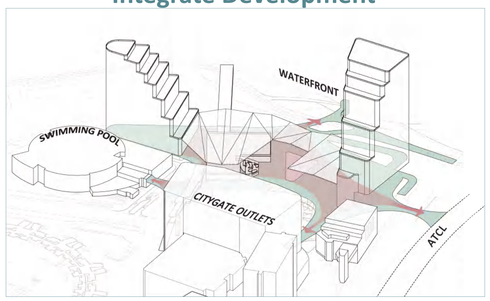

Weave Connectivity

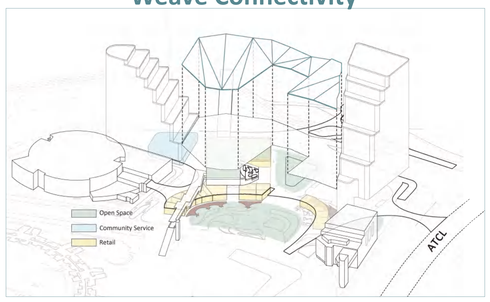

Activate Public Space



Promote Sustainability


9 Aerial View









10 Master Plan

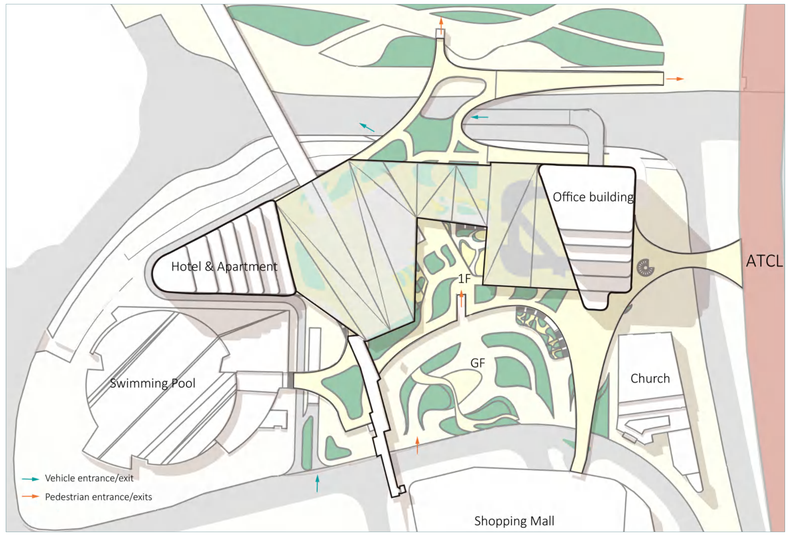


Ground Floor Flow Analysis - Before

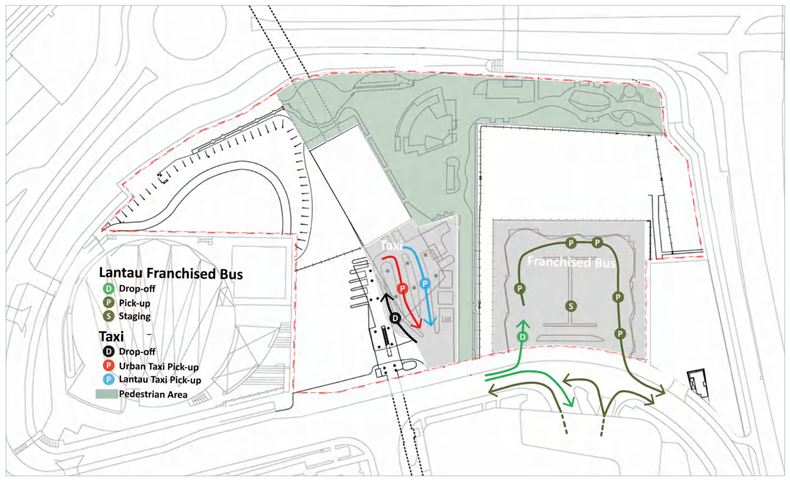


Ground Floor Flow Analysis - After

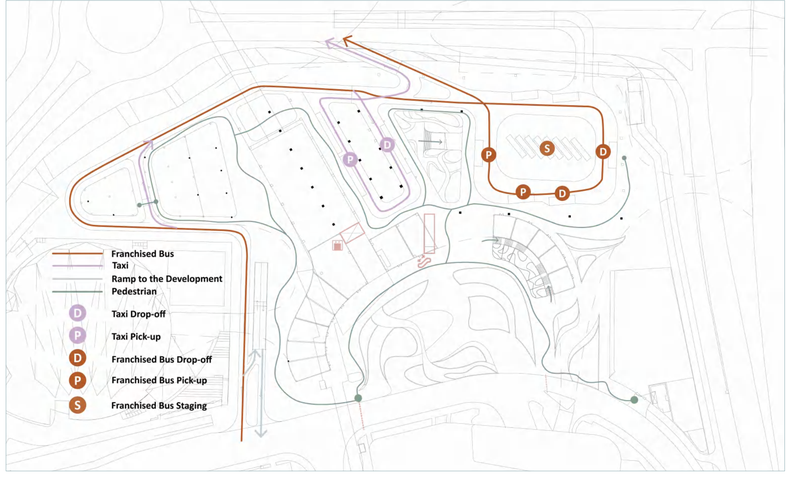


11 Ground Floor Plan - 1:500

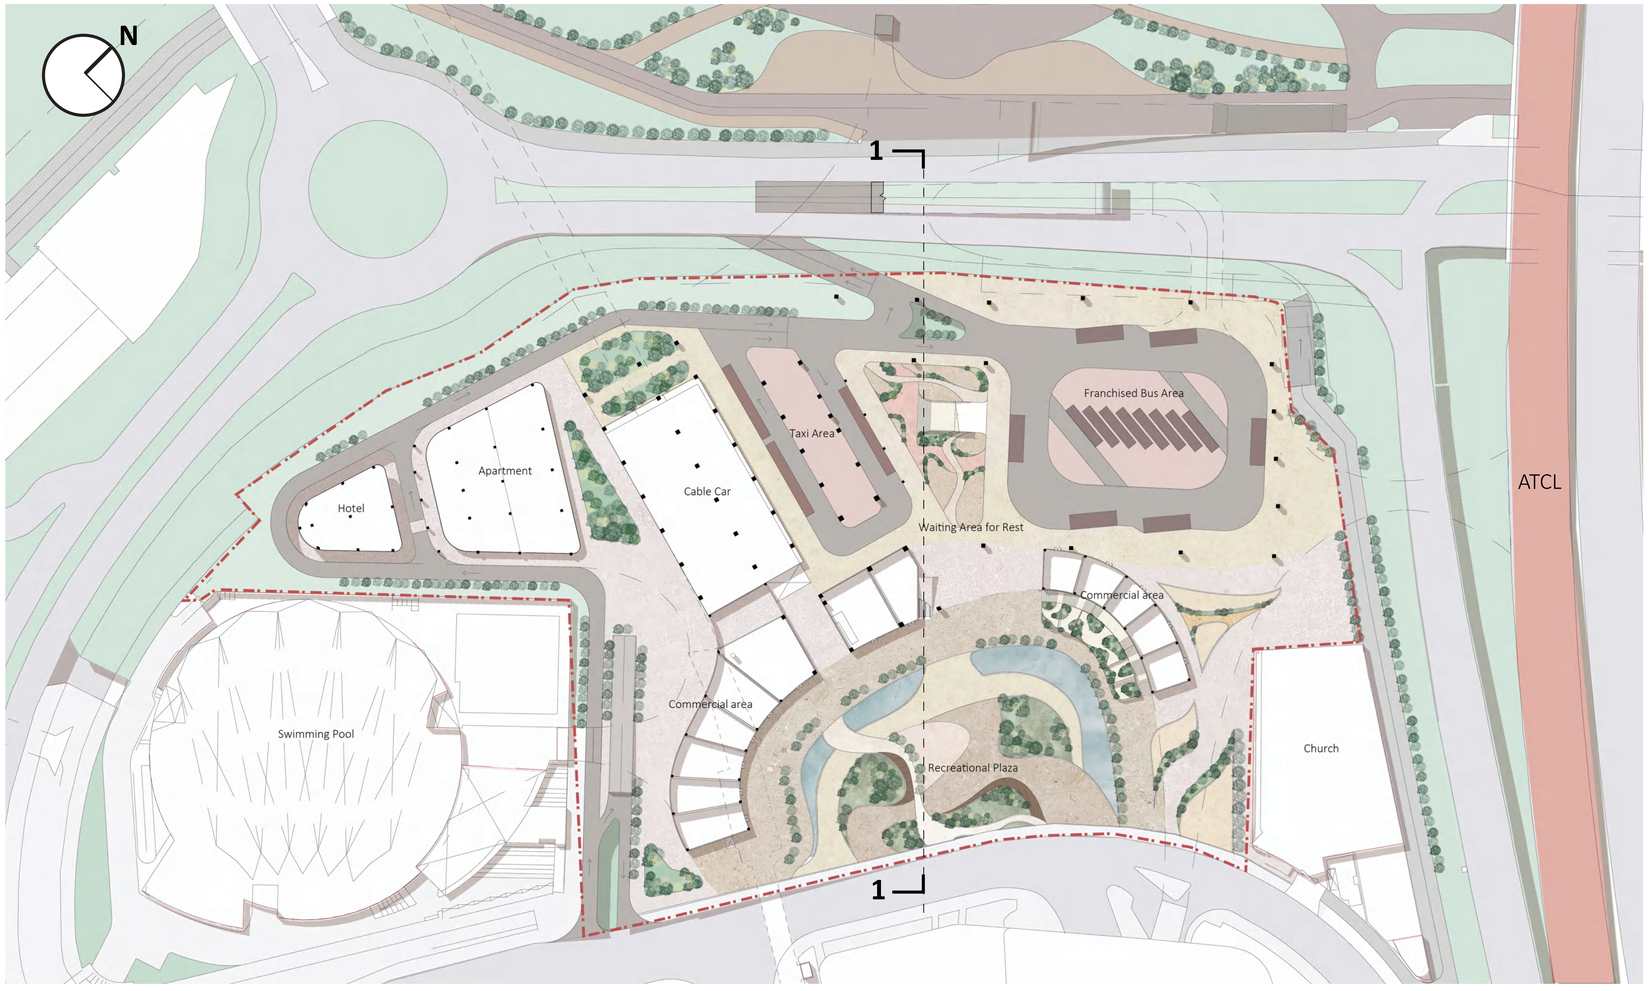

12 JLOS Analysis

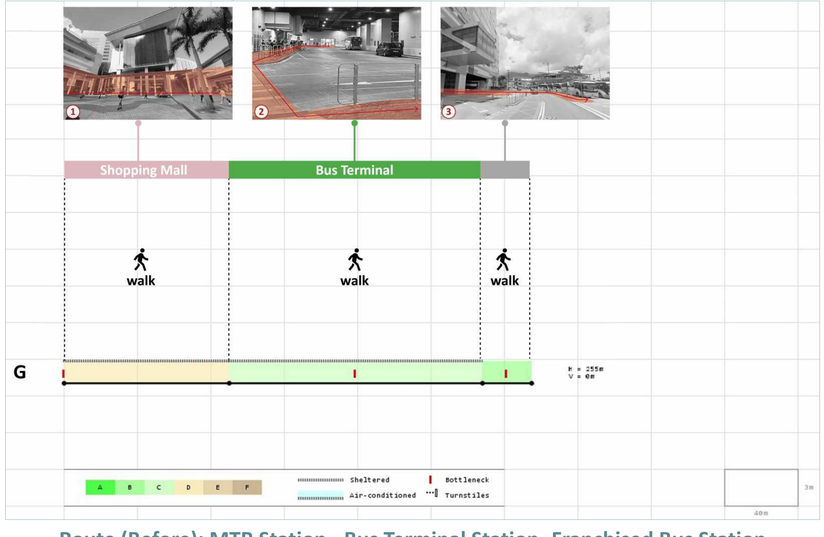


Route (Before): MTR Station - Bus Terminal Station -Franchised Bus Station

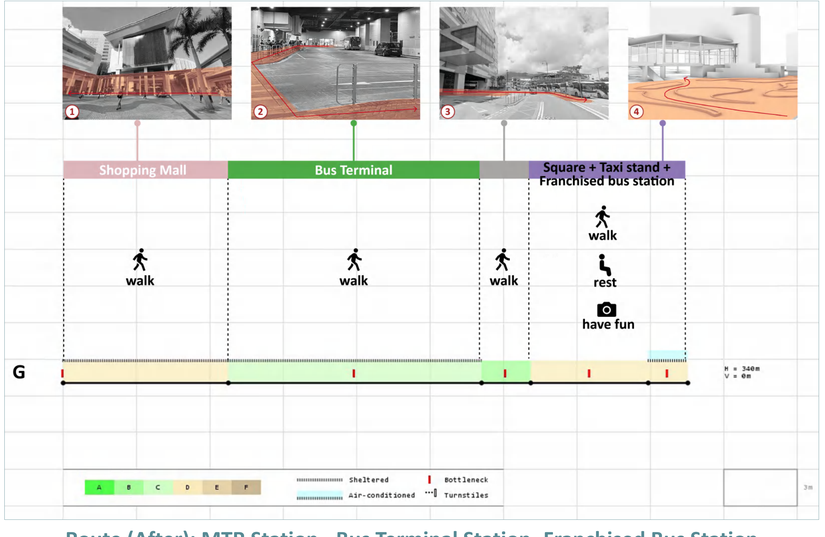


Route (After): MTR Station - Bus Terminal Station -Franchised Bus Station


13 First Floor Plan - 1:500

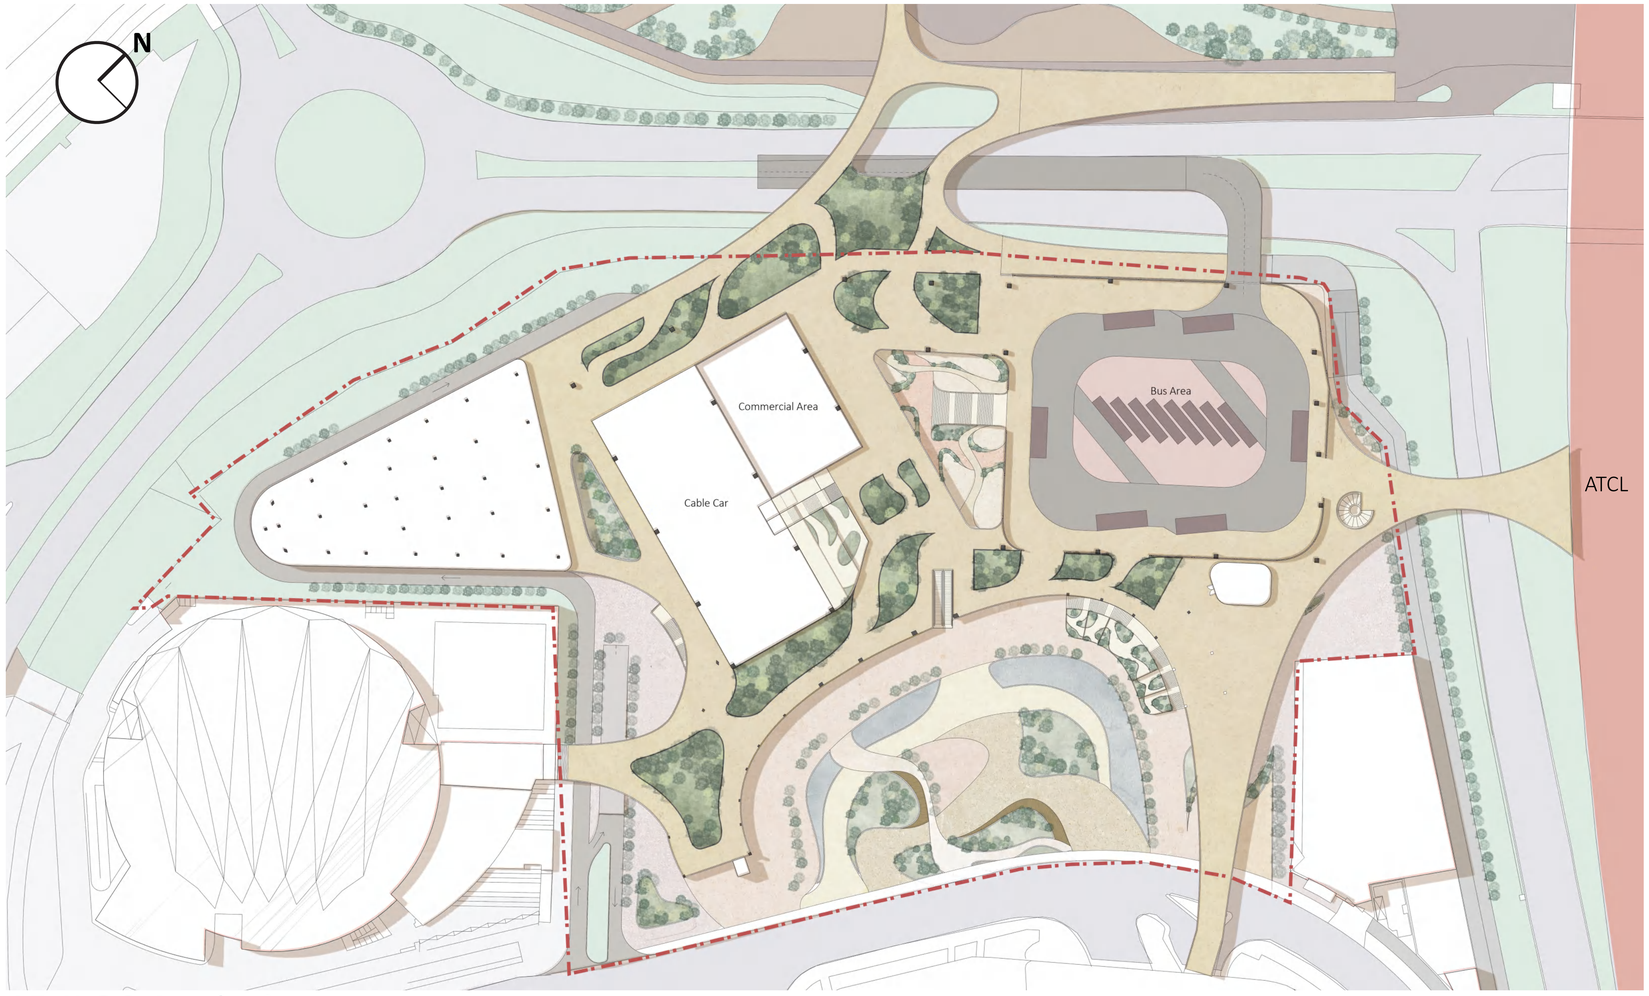


14 Exploded Diagram

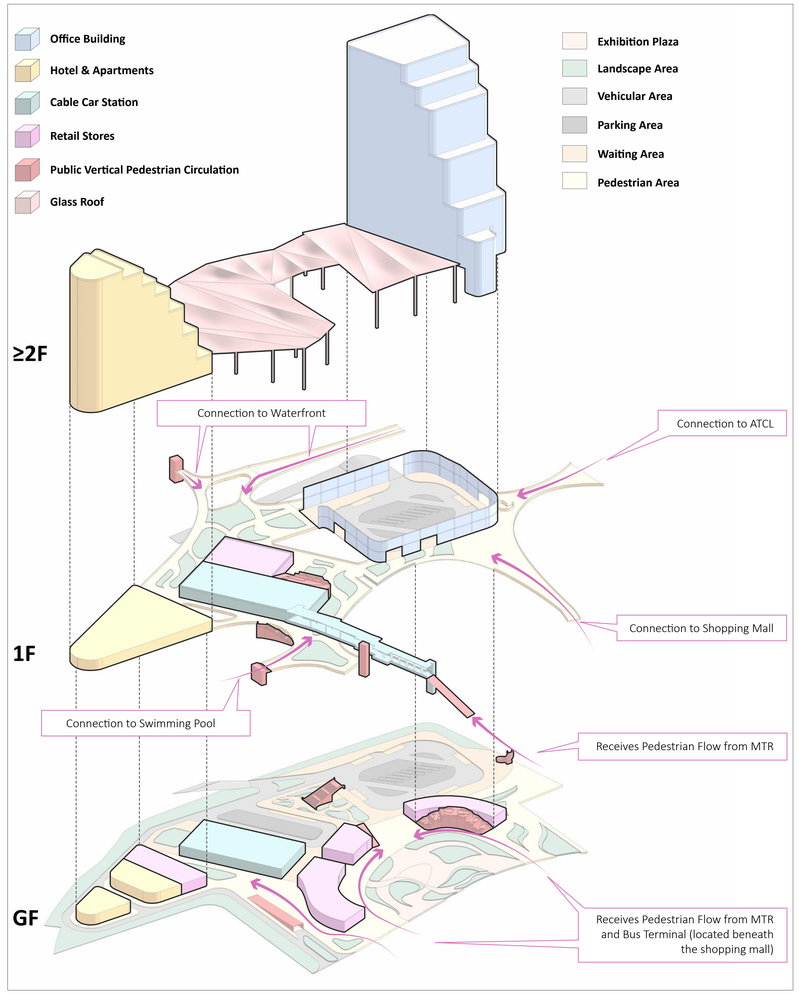

15 JLOS Analysis

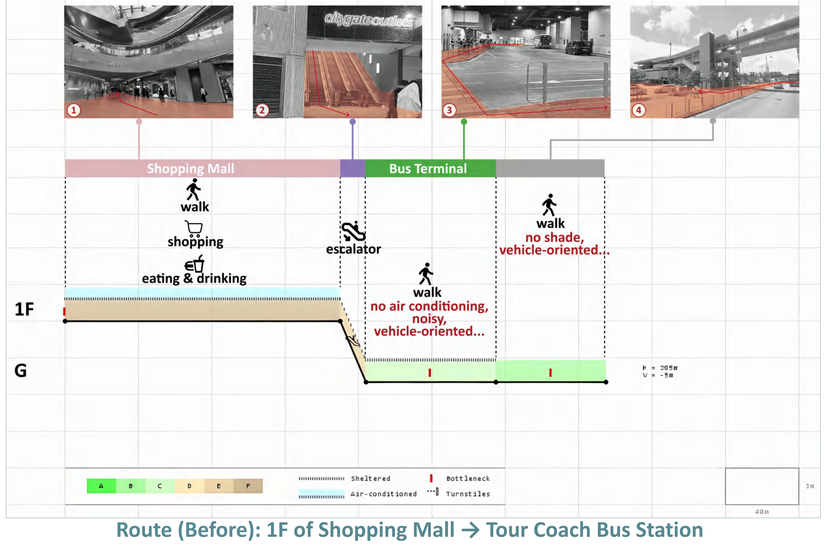


Route (Before): 1F of Shopping Mall → Tour Coach Bus Station

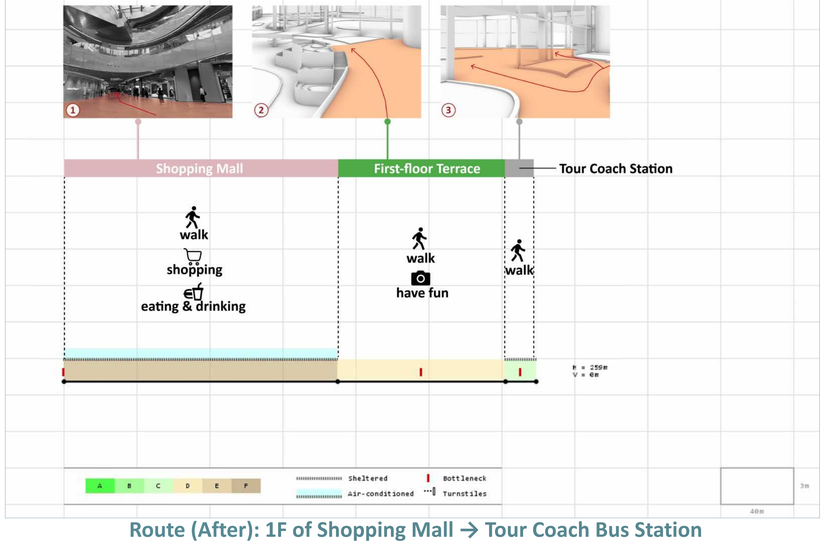

Route (After): 1F of Shopping Mall → Tour Coach Bus Station

First Floor Flow Analysis - After

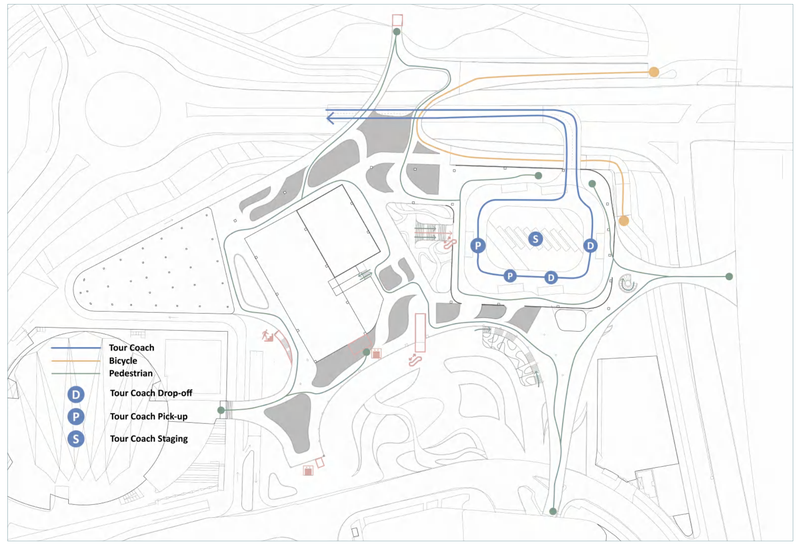

16 Rendering



Franchised Bus Station




Waiting area + Ground floor to the first-floor platform



From the first-floor platform to the cable car station

17 Detailed Plan - 1:200

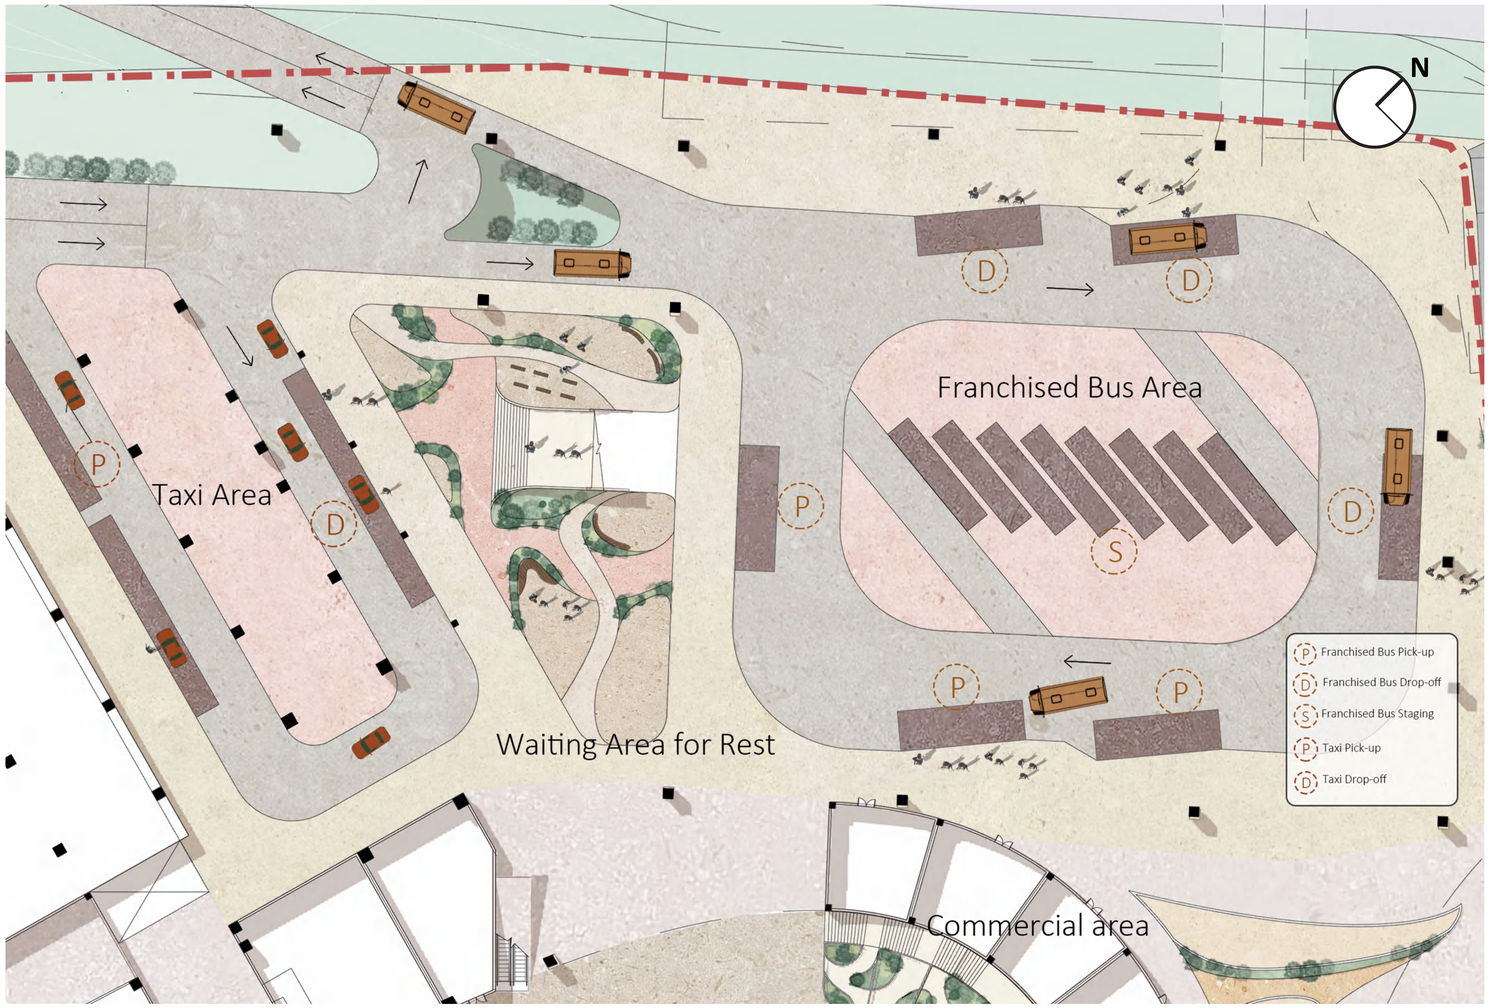

18 Ecological Strategy (Section 1-1)

